




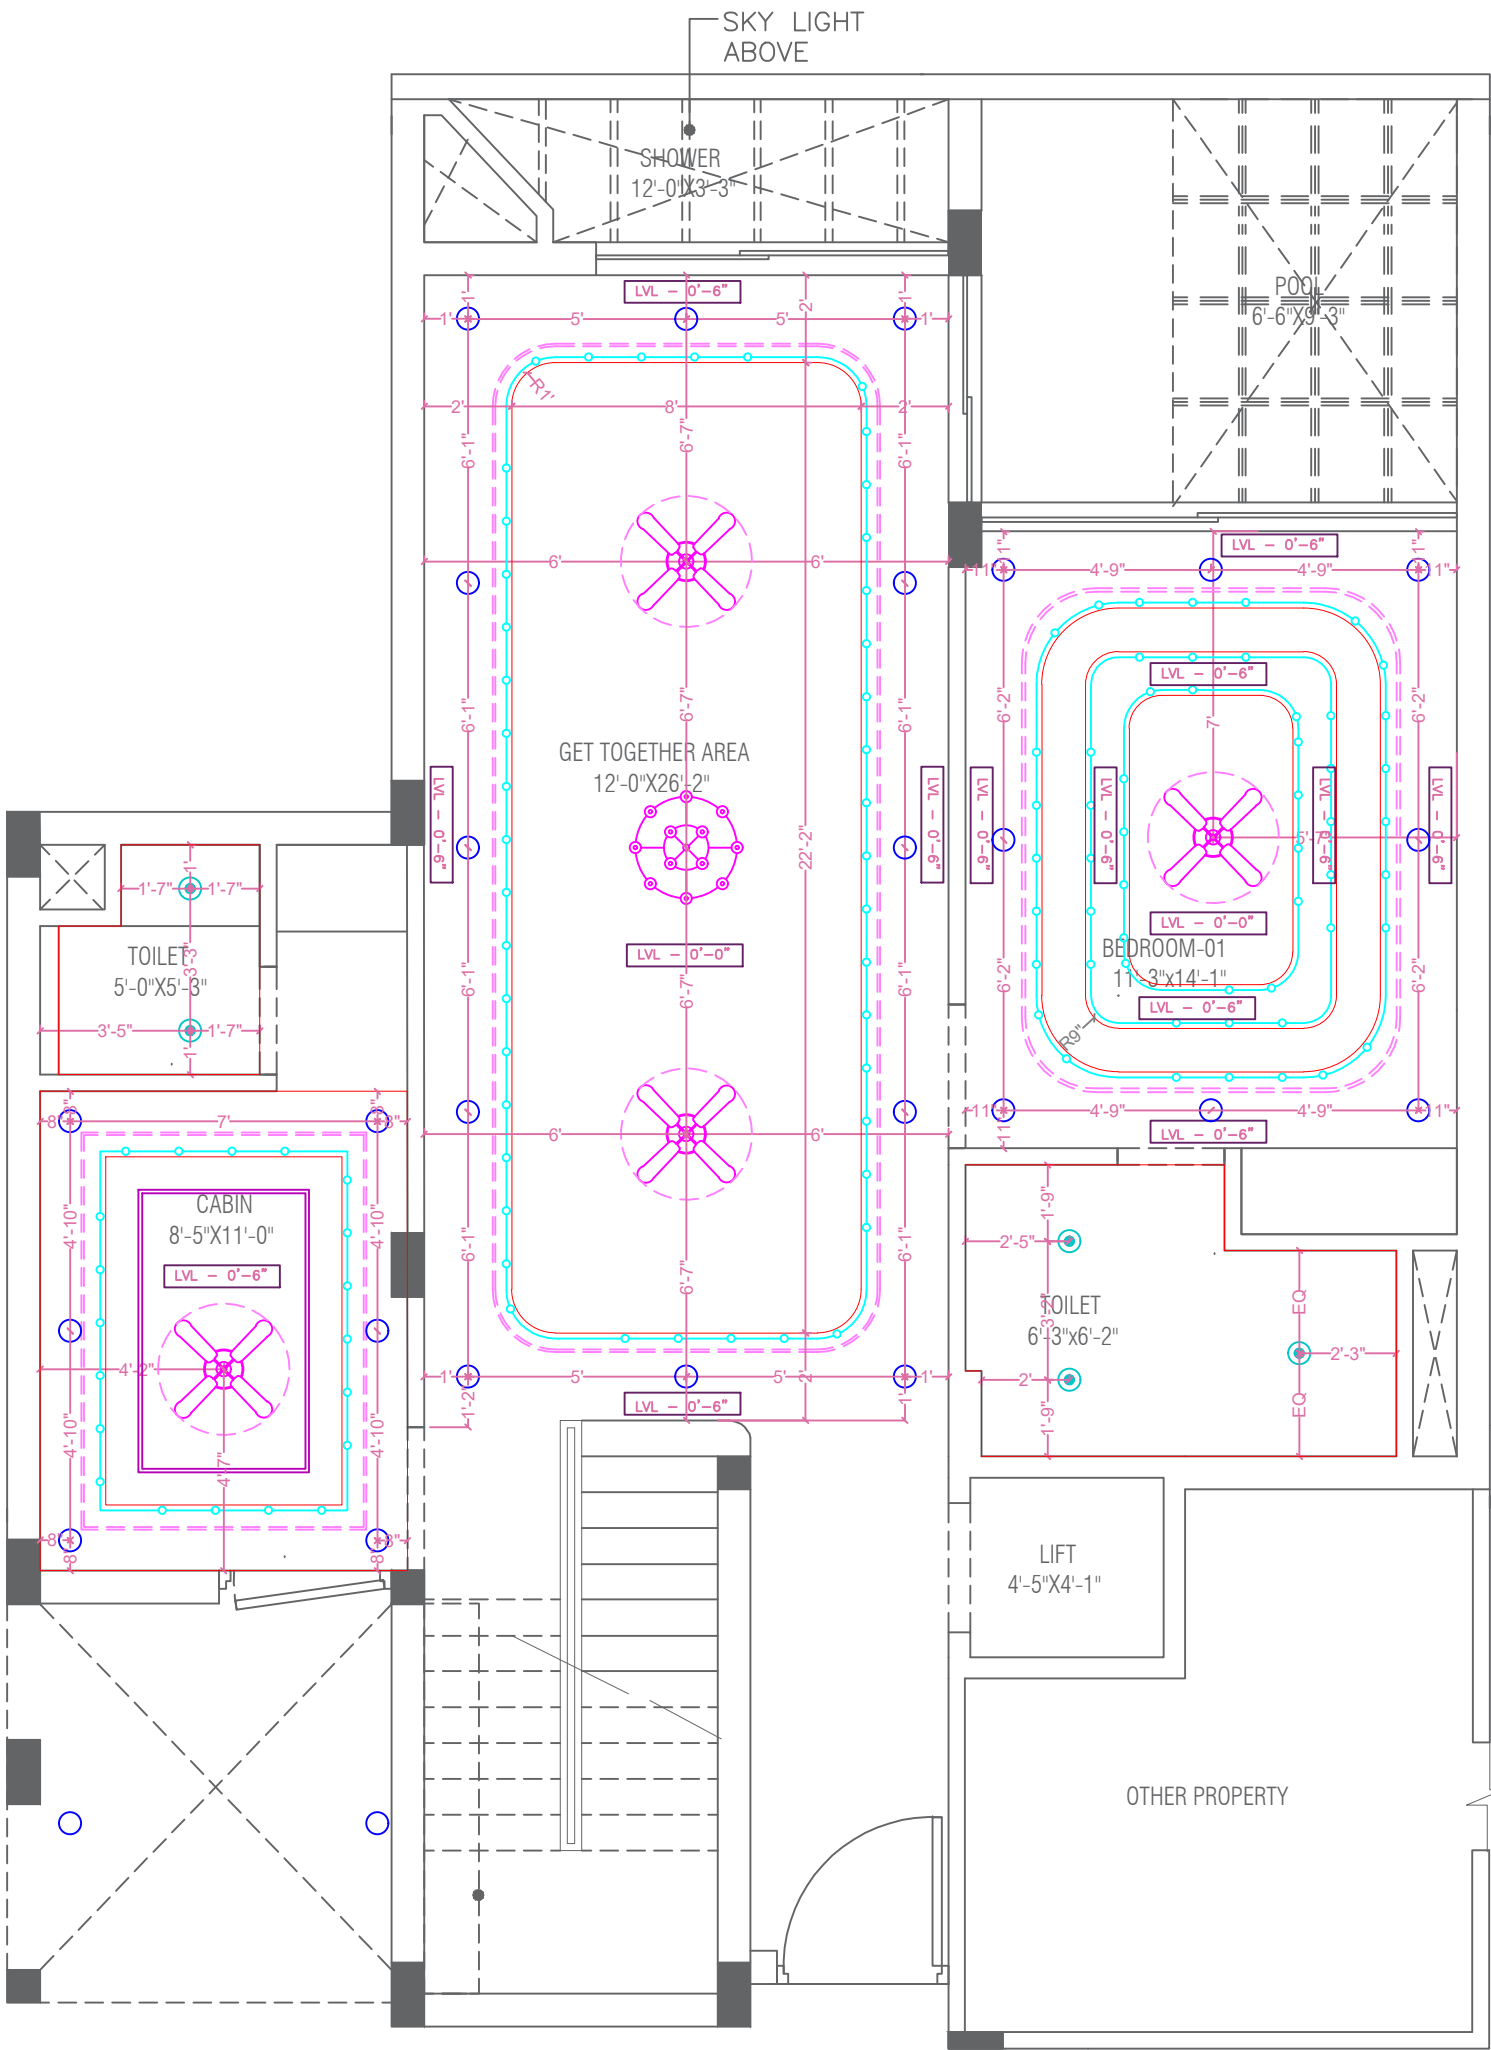

LEGEND		
SYMBOL	WATT	QTY
	5W	16
	7W	52
	12W	02
	PROFILE LIGHT	117'-0" RUNNING
	600Ø	01
	900Ø	06
	CHANDE- LIER	01

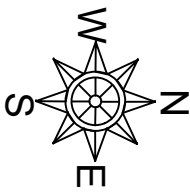

01 BEDROOM-1
REFERENCE IMAGE

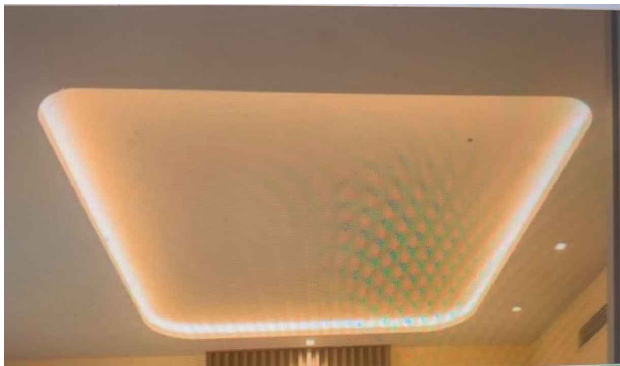

02 LIVING AREA
REFERENCE IMAGE



03 CABIN
REFERENCE IMAGE

ARCHITECTS



Architects, Interior Designer, Landscape Designer, & Structural Designer
Head. Off: F-52, 1st Floor, Near Gurdwara, Madhu Vihar, JP Extension, Delhi-110092

Architect:
AR. PRABHAT ARYA

Sign:

Date:

Project Title:

**RESIDENCE
AT
RISE VILLA**

Drawing Title:

**BASEMENT
CEILING LAYOUT PLAN**

Scale:

NTS

Date:

2026.05.07

Proj No:

—

Rev. No:

—

File Name:

—

Drawn:

SUMIT

Checked:


Ar. Yojna

Dwg No:


RCP_1001

Rev. Date:

—

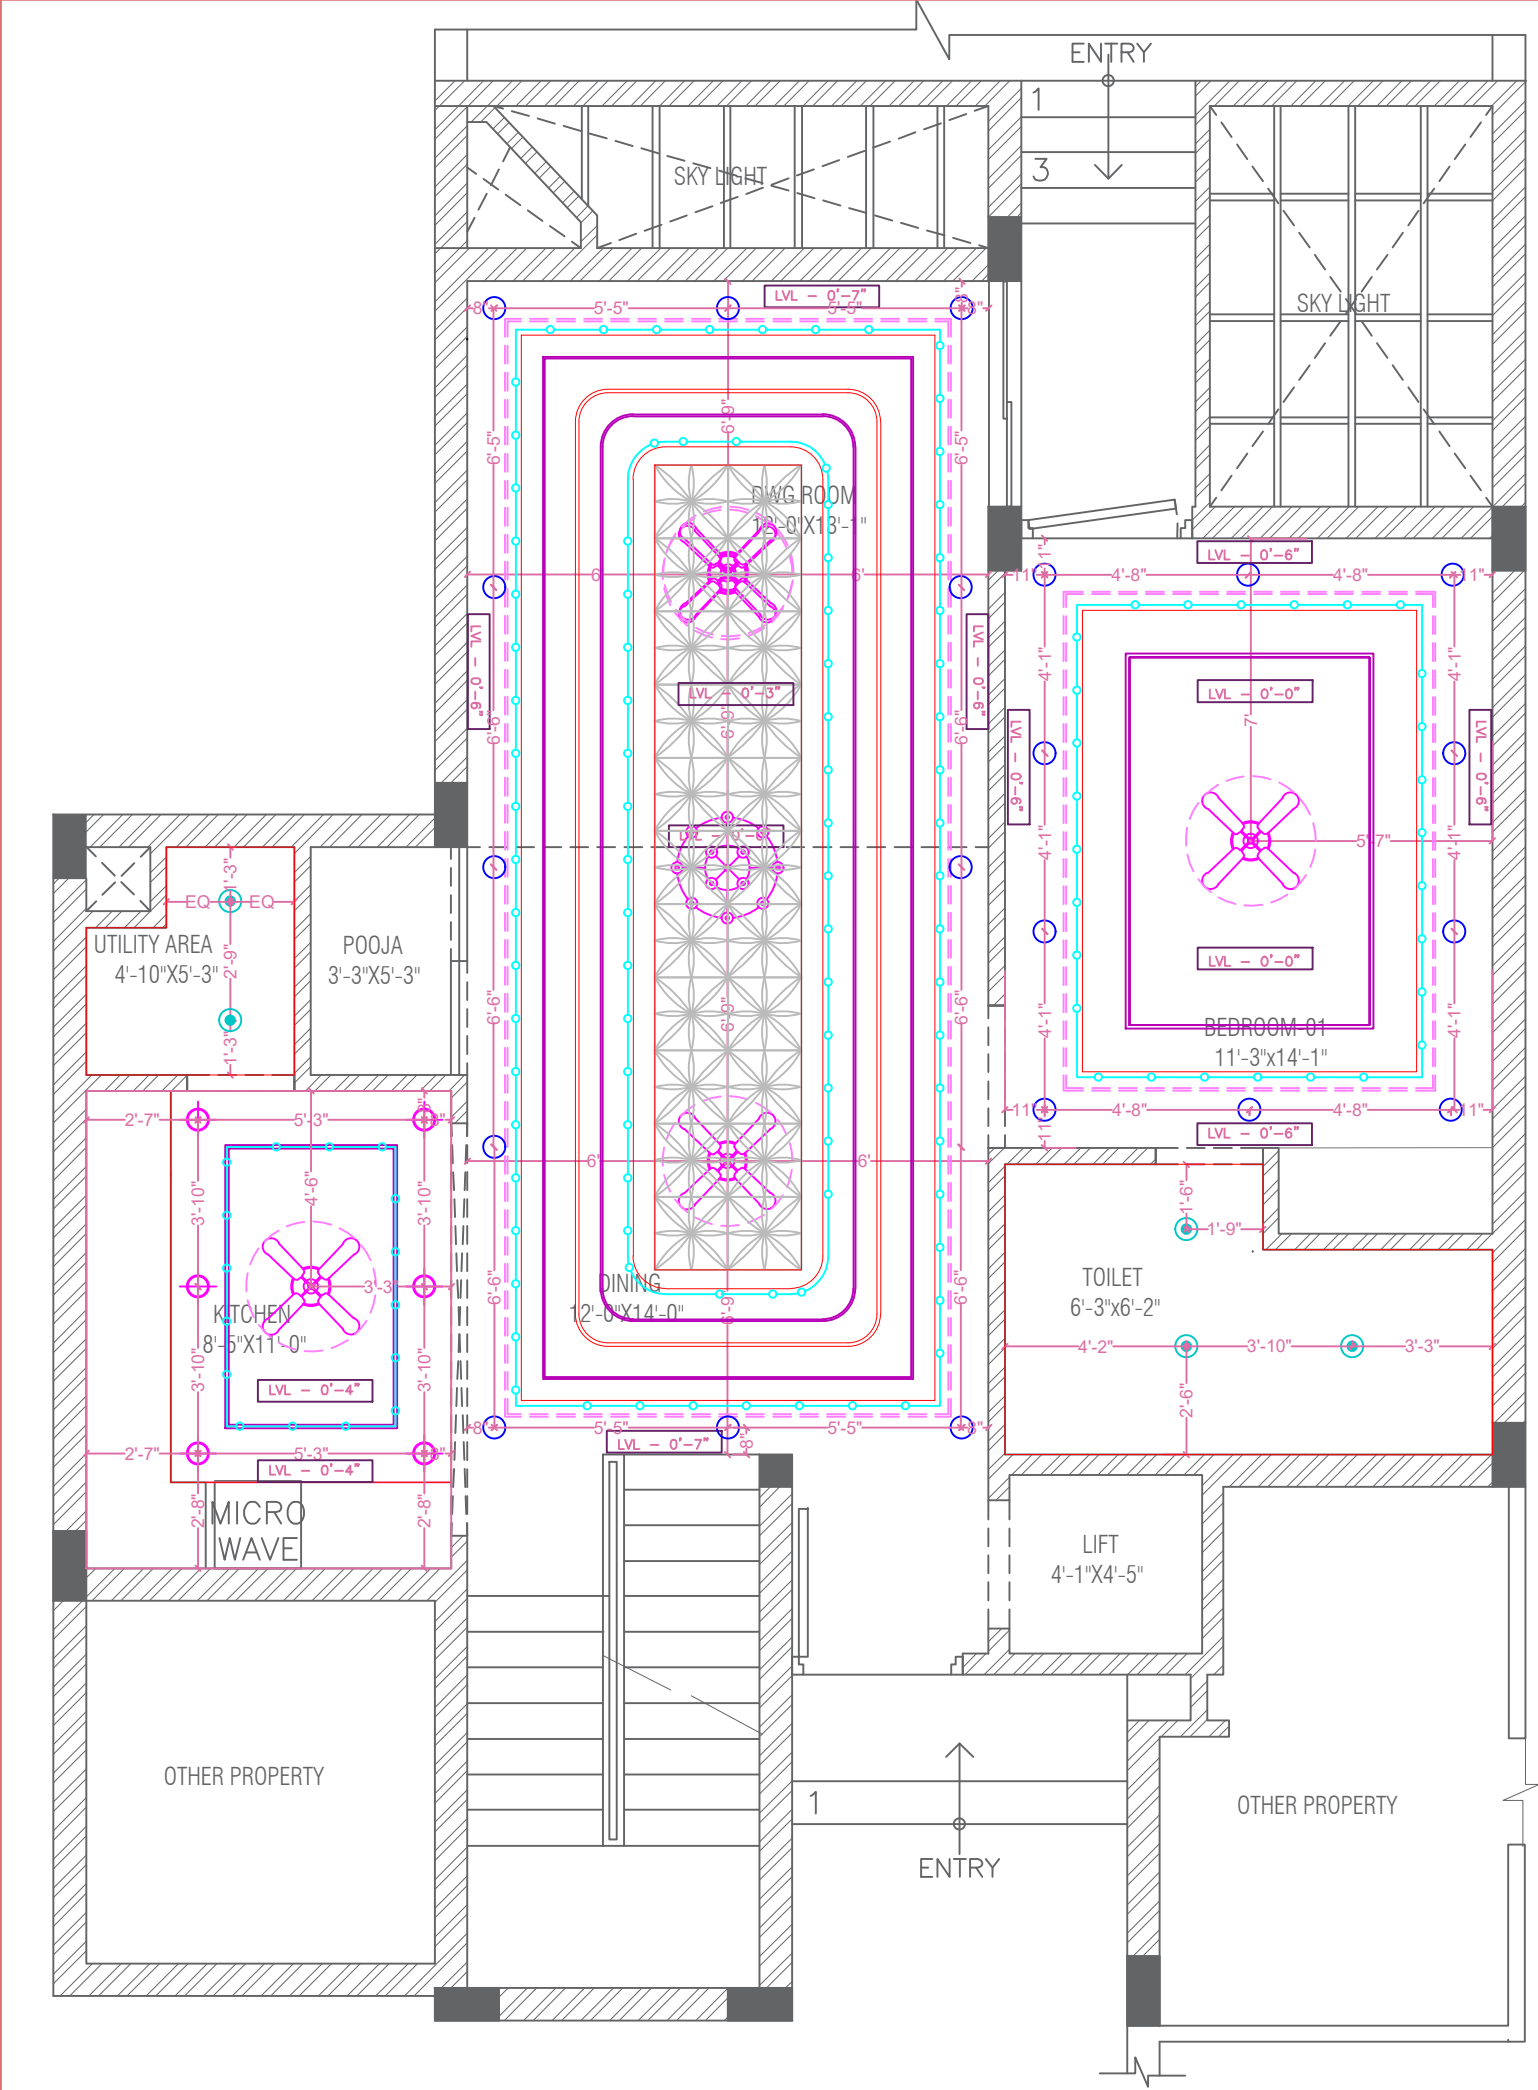

LEGEND		
SYMBOL	WATT	QTY
	5W	16
	7W	52
	12W	02
	PROFILE LIGHT	117'-0" RUNNING
	6000	01
	9000	06
	CHANDE-LIER	01

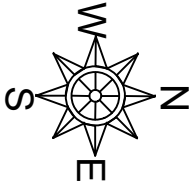

01 LIVING AREA
REFERENCE IMAGE




02 BEDROOM
REFERENCE IMAGE




03 KITCHEN
REFERENCE IMAGE

ARCHITECTS ARCHITECTSHIVE REDEFINING THE LIMITS OF ARCHITECTURE Architects, Interior Designer, Landscape Designer, & Structural Designer Head. Off: F-52, 1st Floor, Near Gurudwara, Madhu Vihar, JP Extension, Delhi-110092	Architect: AR. PRABHAT ARYA		Project Title: RESIDENCE AT RISE VILLA		Drawing Title: GROUND FLOOR CEILING LAYOUT PLAN	Scale: NTS	Drawn: SUMIT
	Sign:		Date:			Date: 2026.05.07	Checked: Ar. Yojna
						Proj No: -	Dwg No: RCP_1002
						Rev. No: -	Rev. Date: -
						File Name: -	

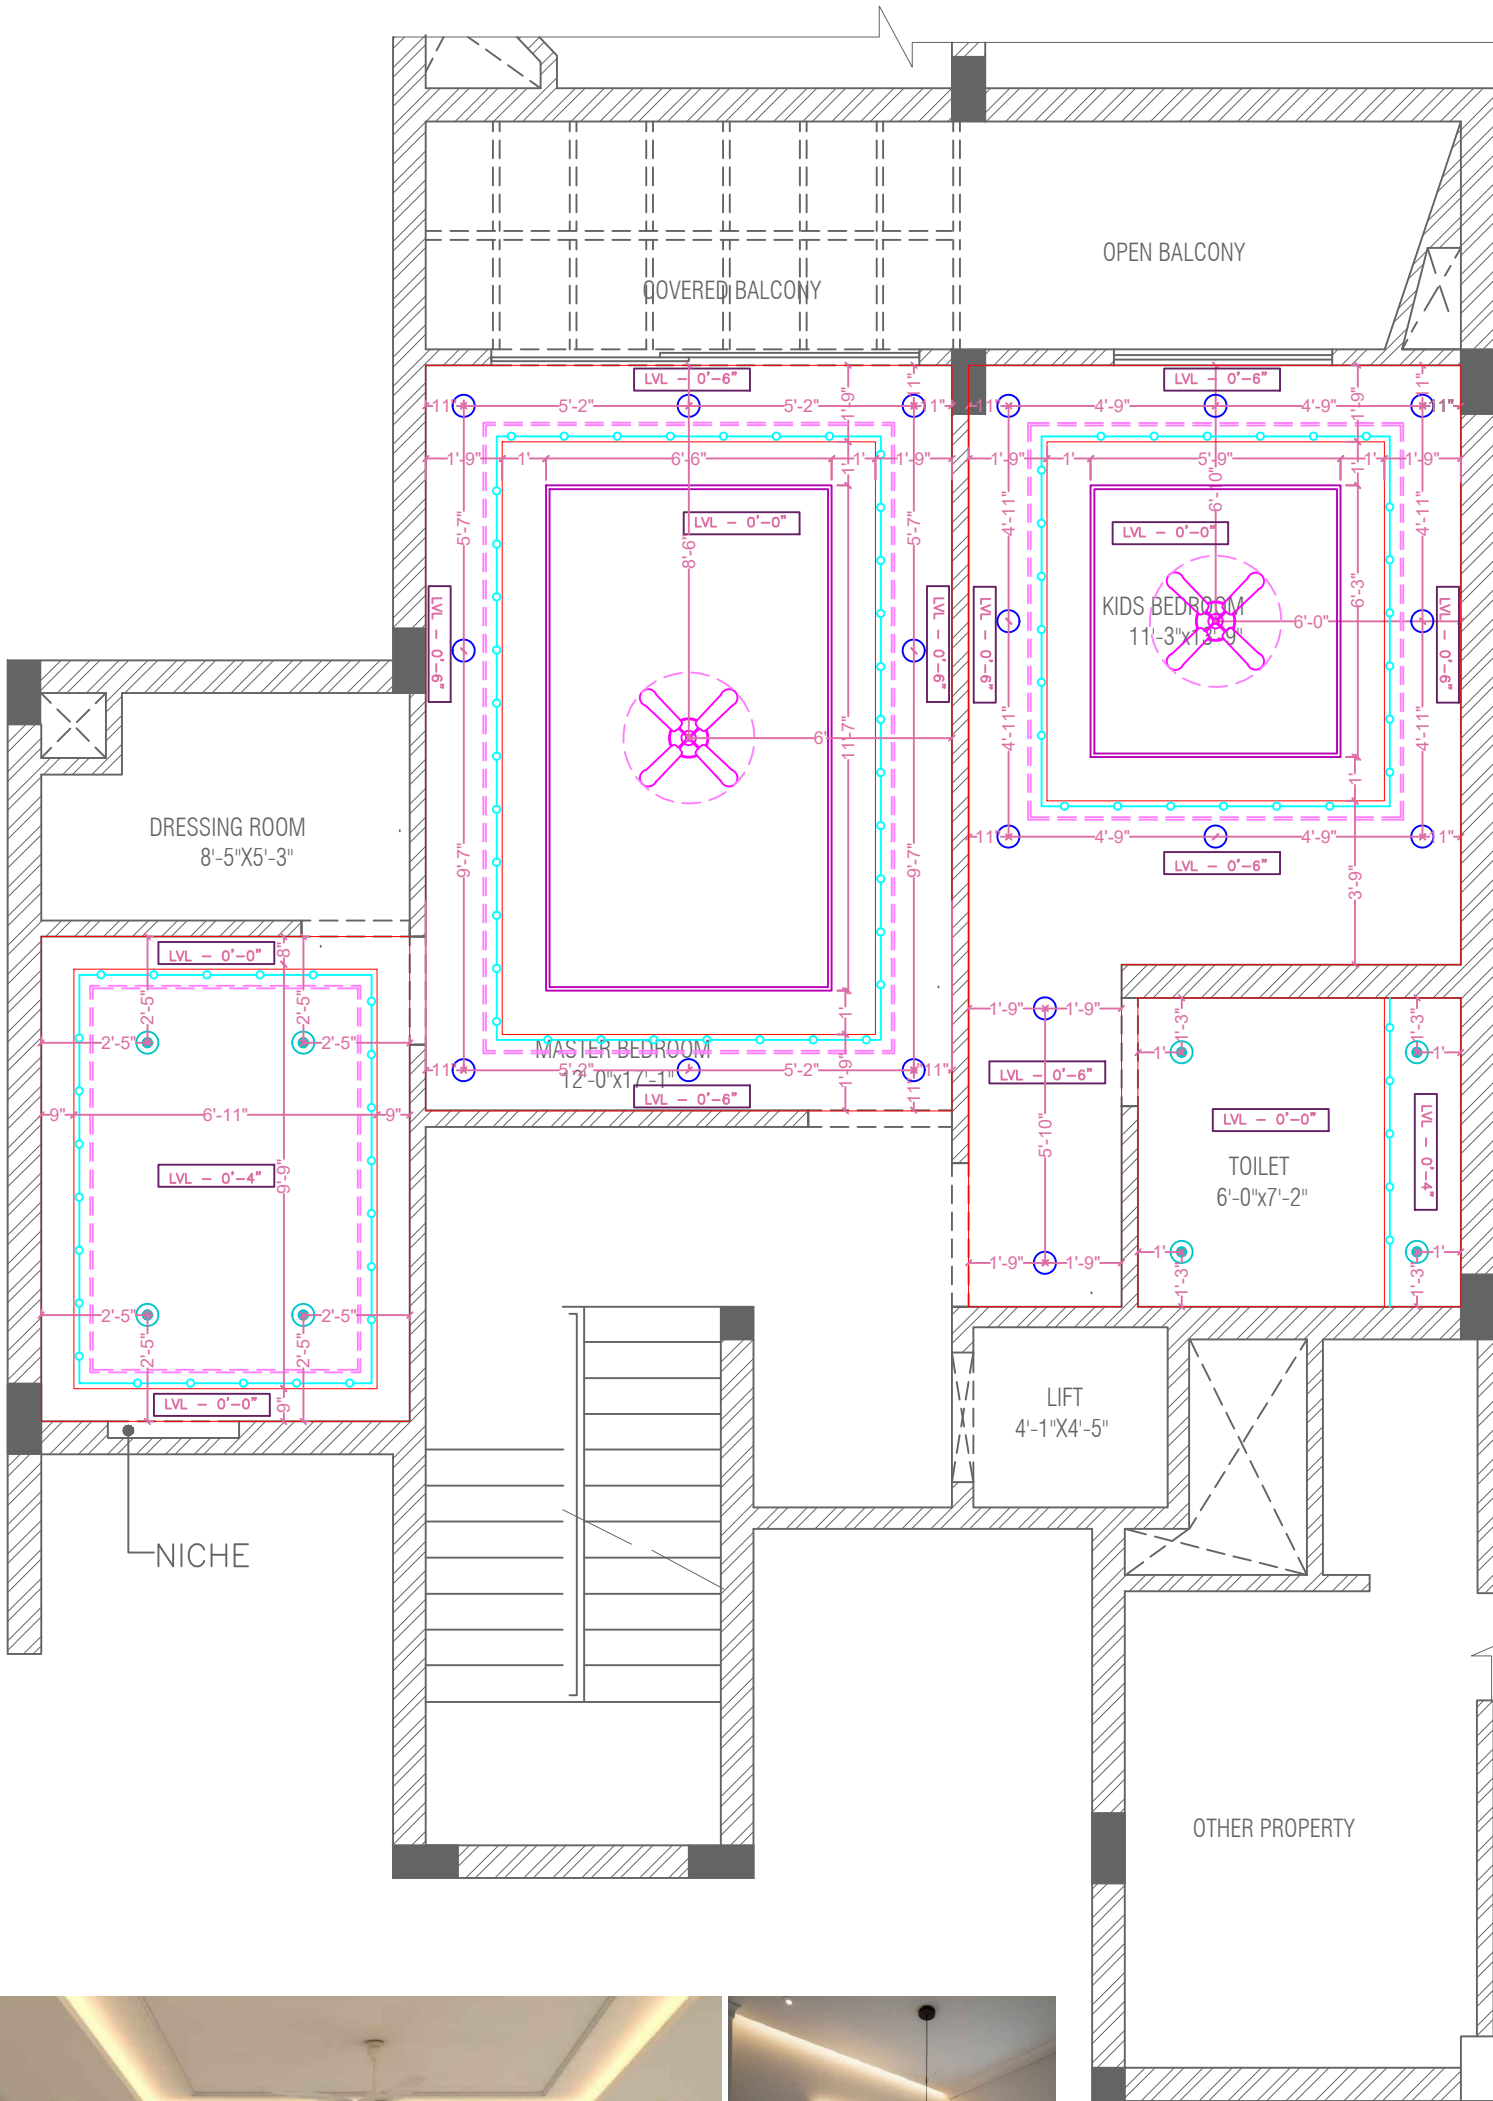


LEGEND		
SYMBOL	WATT	QTY
	5W	16
	7W	52
	12W	02
	PROFILE LIGHT	117'-0" RUNNING
	6000	01
	9000	06
	CHANDE- LIER	01

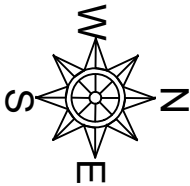



01 MASTER BEDROOM
REFERENCE IMAGE

02 TOILET
REFERENCE IMAGE

ARCHITECTS ARCHITECTSHIVE REDEFINING THE LIMITS OF ARCHITECTURE Architects, Interior Designer, Landscape Designer, & Structural Designer Head. Off: F-52, 1st Floor, Near Gurudwara, Madhu Vihar, JP Extension, Delhi-110092	Architect: AR. PRABHAT ARYA		Project Title: RESIDENCE AT RISE VILLA		Drawing Title: FIRST FLOOR CEILING LAYOUT PLAN		Scale: NTS	Drawn: SUMIT
	Sign:		Date:		Date: 2026.05.07		Proj No: —	Checked: Ar. Yojna
					Rev. No:		Dwg No: RCP_1003	Rev. Date:
					File Name:		—	—

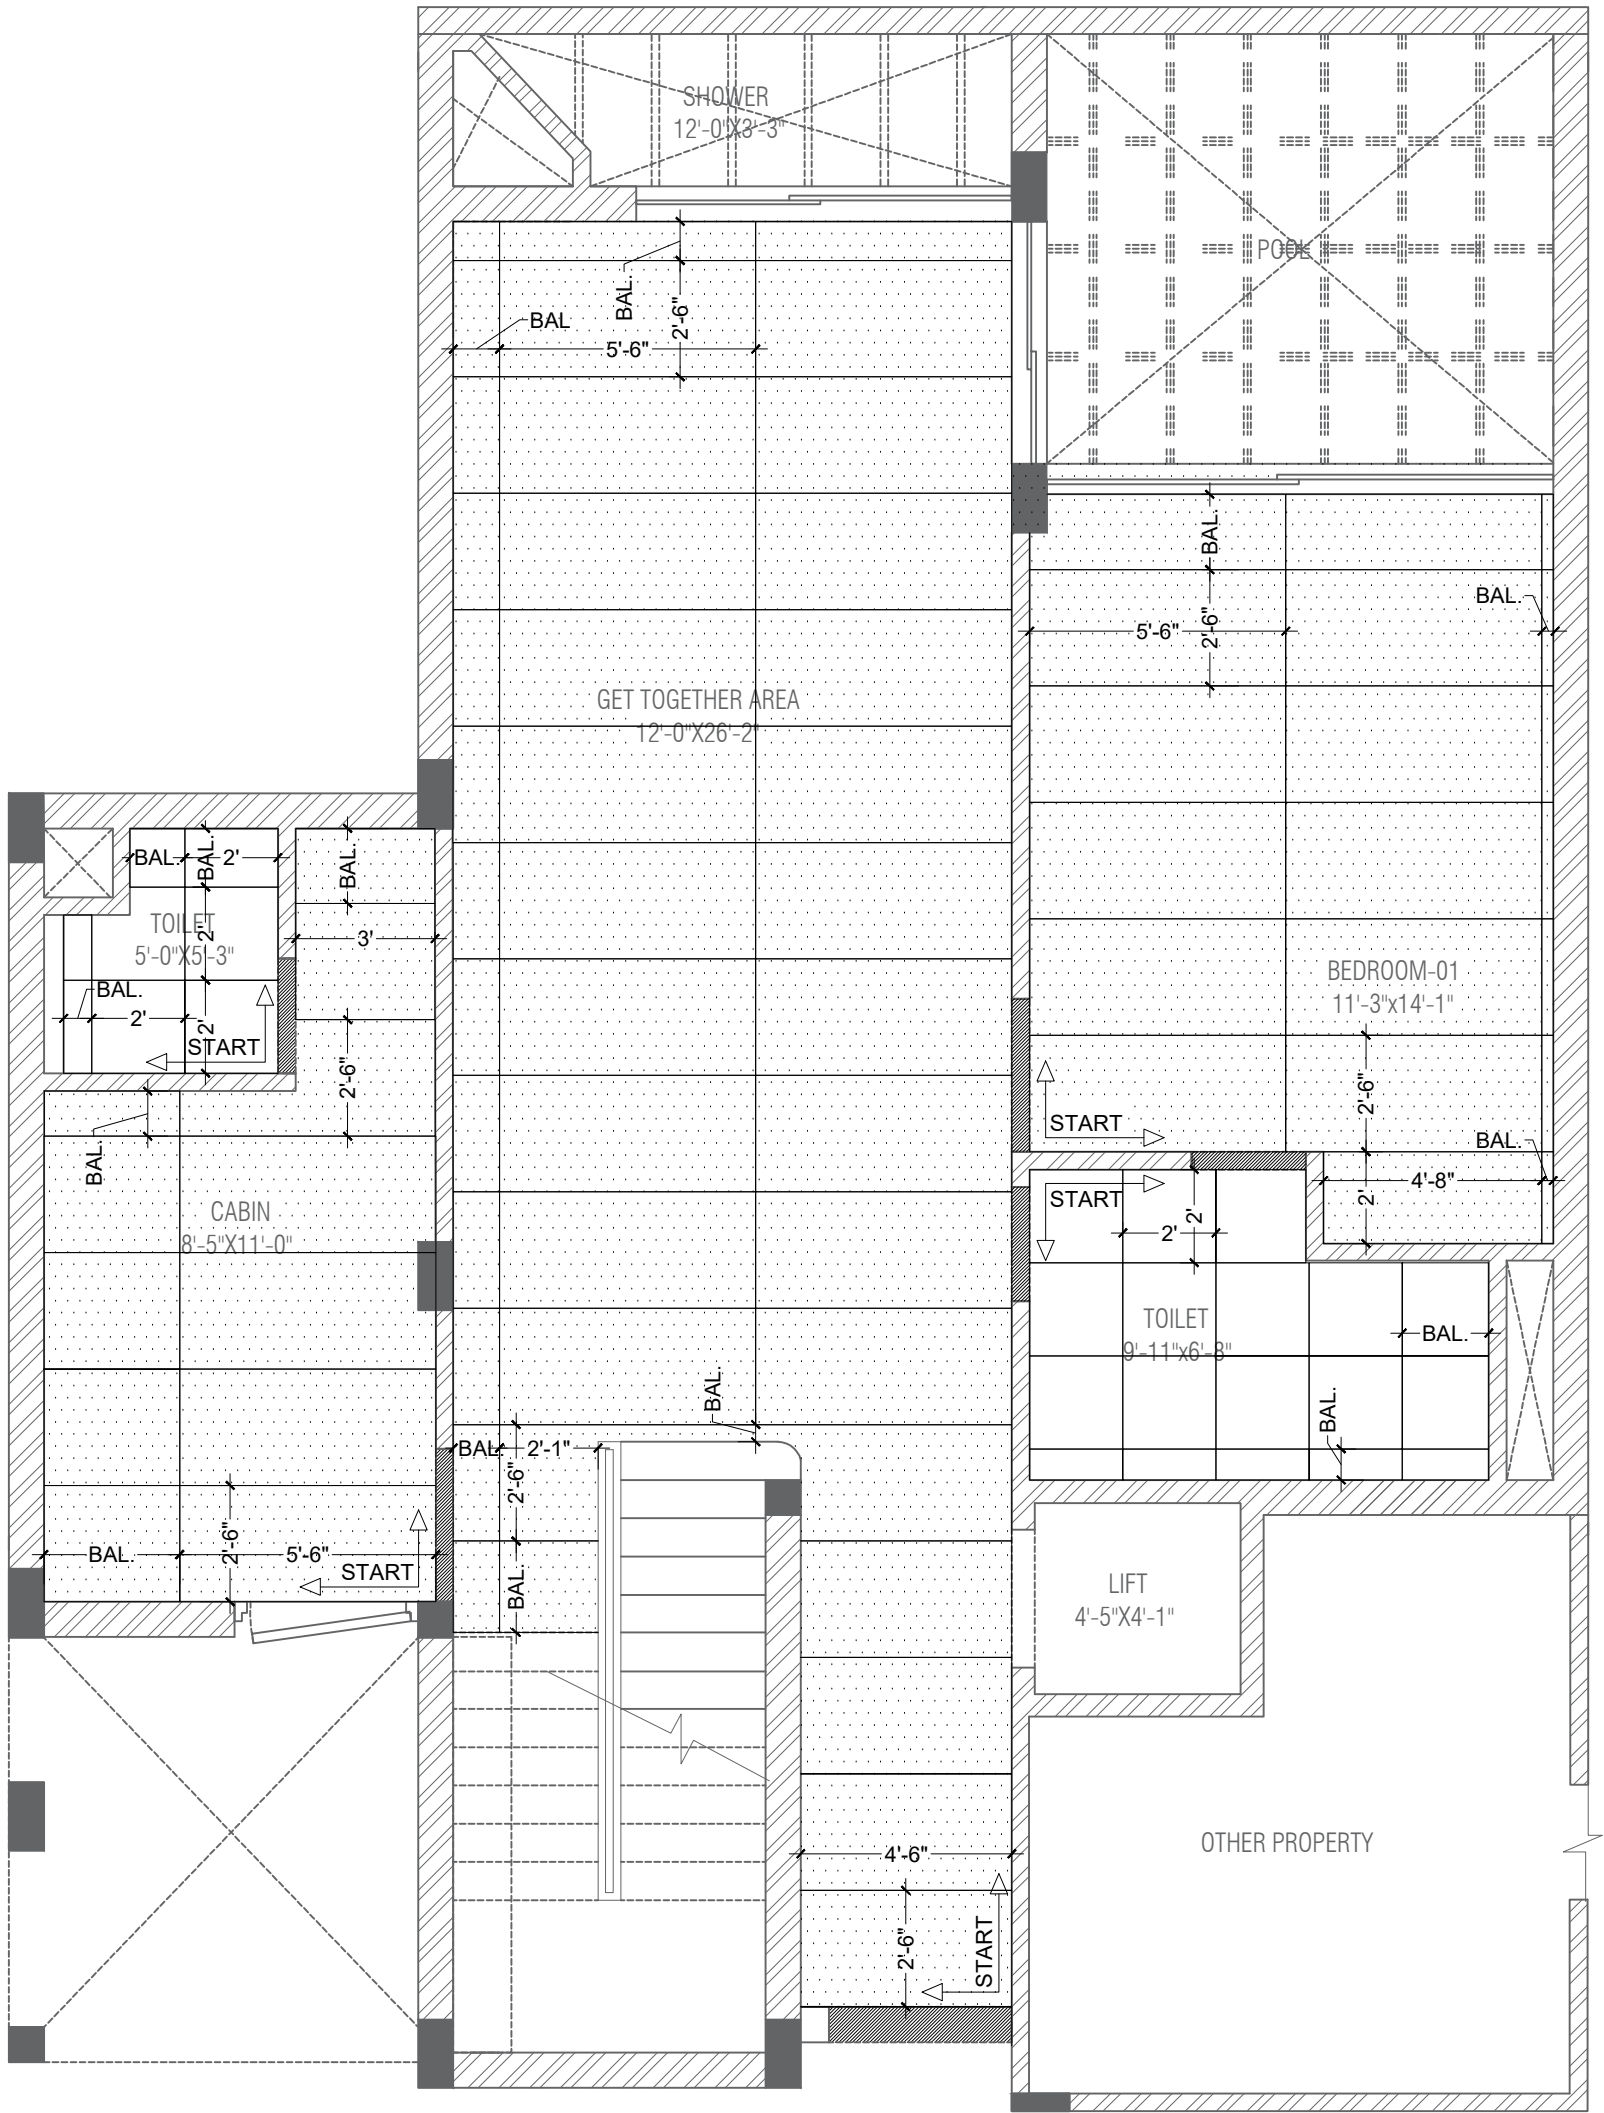

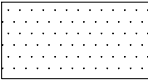LEGEND		
S,NO	TILES	SIZE
1		2'-6" x "5'-6"
2		2' x 2'

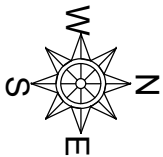

ARCHITECTS



Architects, Interior Designer, Landscape Designer, & Structural Designer
Head. Off: F-52, 1st Floor, Near Gurdwara, Madhu Vihar, J.P. Extension, Delhi-110092

Architect:

AR. PRABHAT ARYA

Sign:

Date:

Project Title:

RESIDENCE
AT
RISE VILLA

Drawing Title:

BASEMENT
PLUMBING LAYOUT PLAN

Scale:

NTS

Date:

2026.05.08

Proj No:

—

Rev. No:

—

File Name:

—

Drawn:

SUMIT

Checked:


Ar. Yojna

Dwg No:


FL_1001

Rev. Date:

—

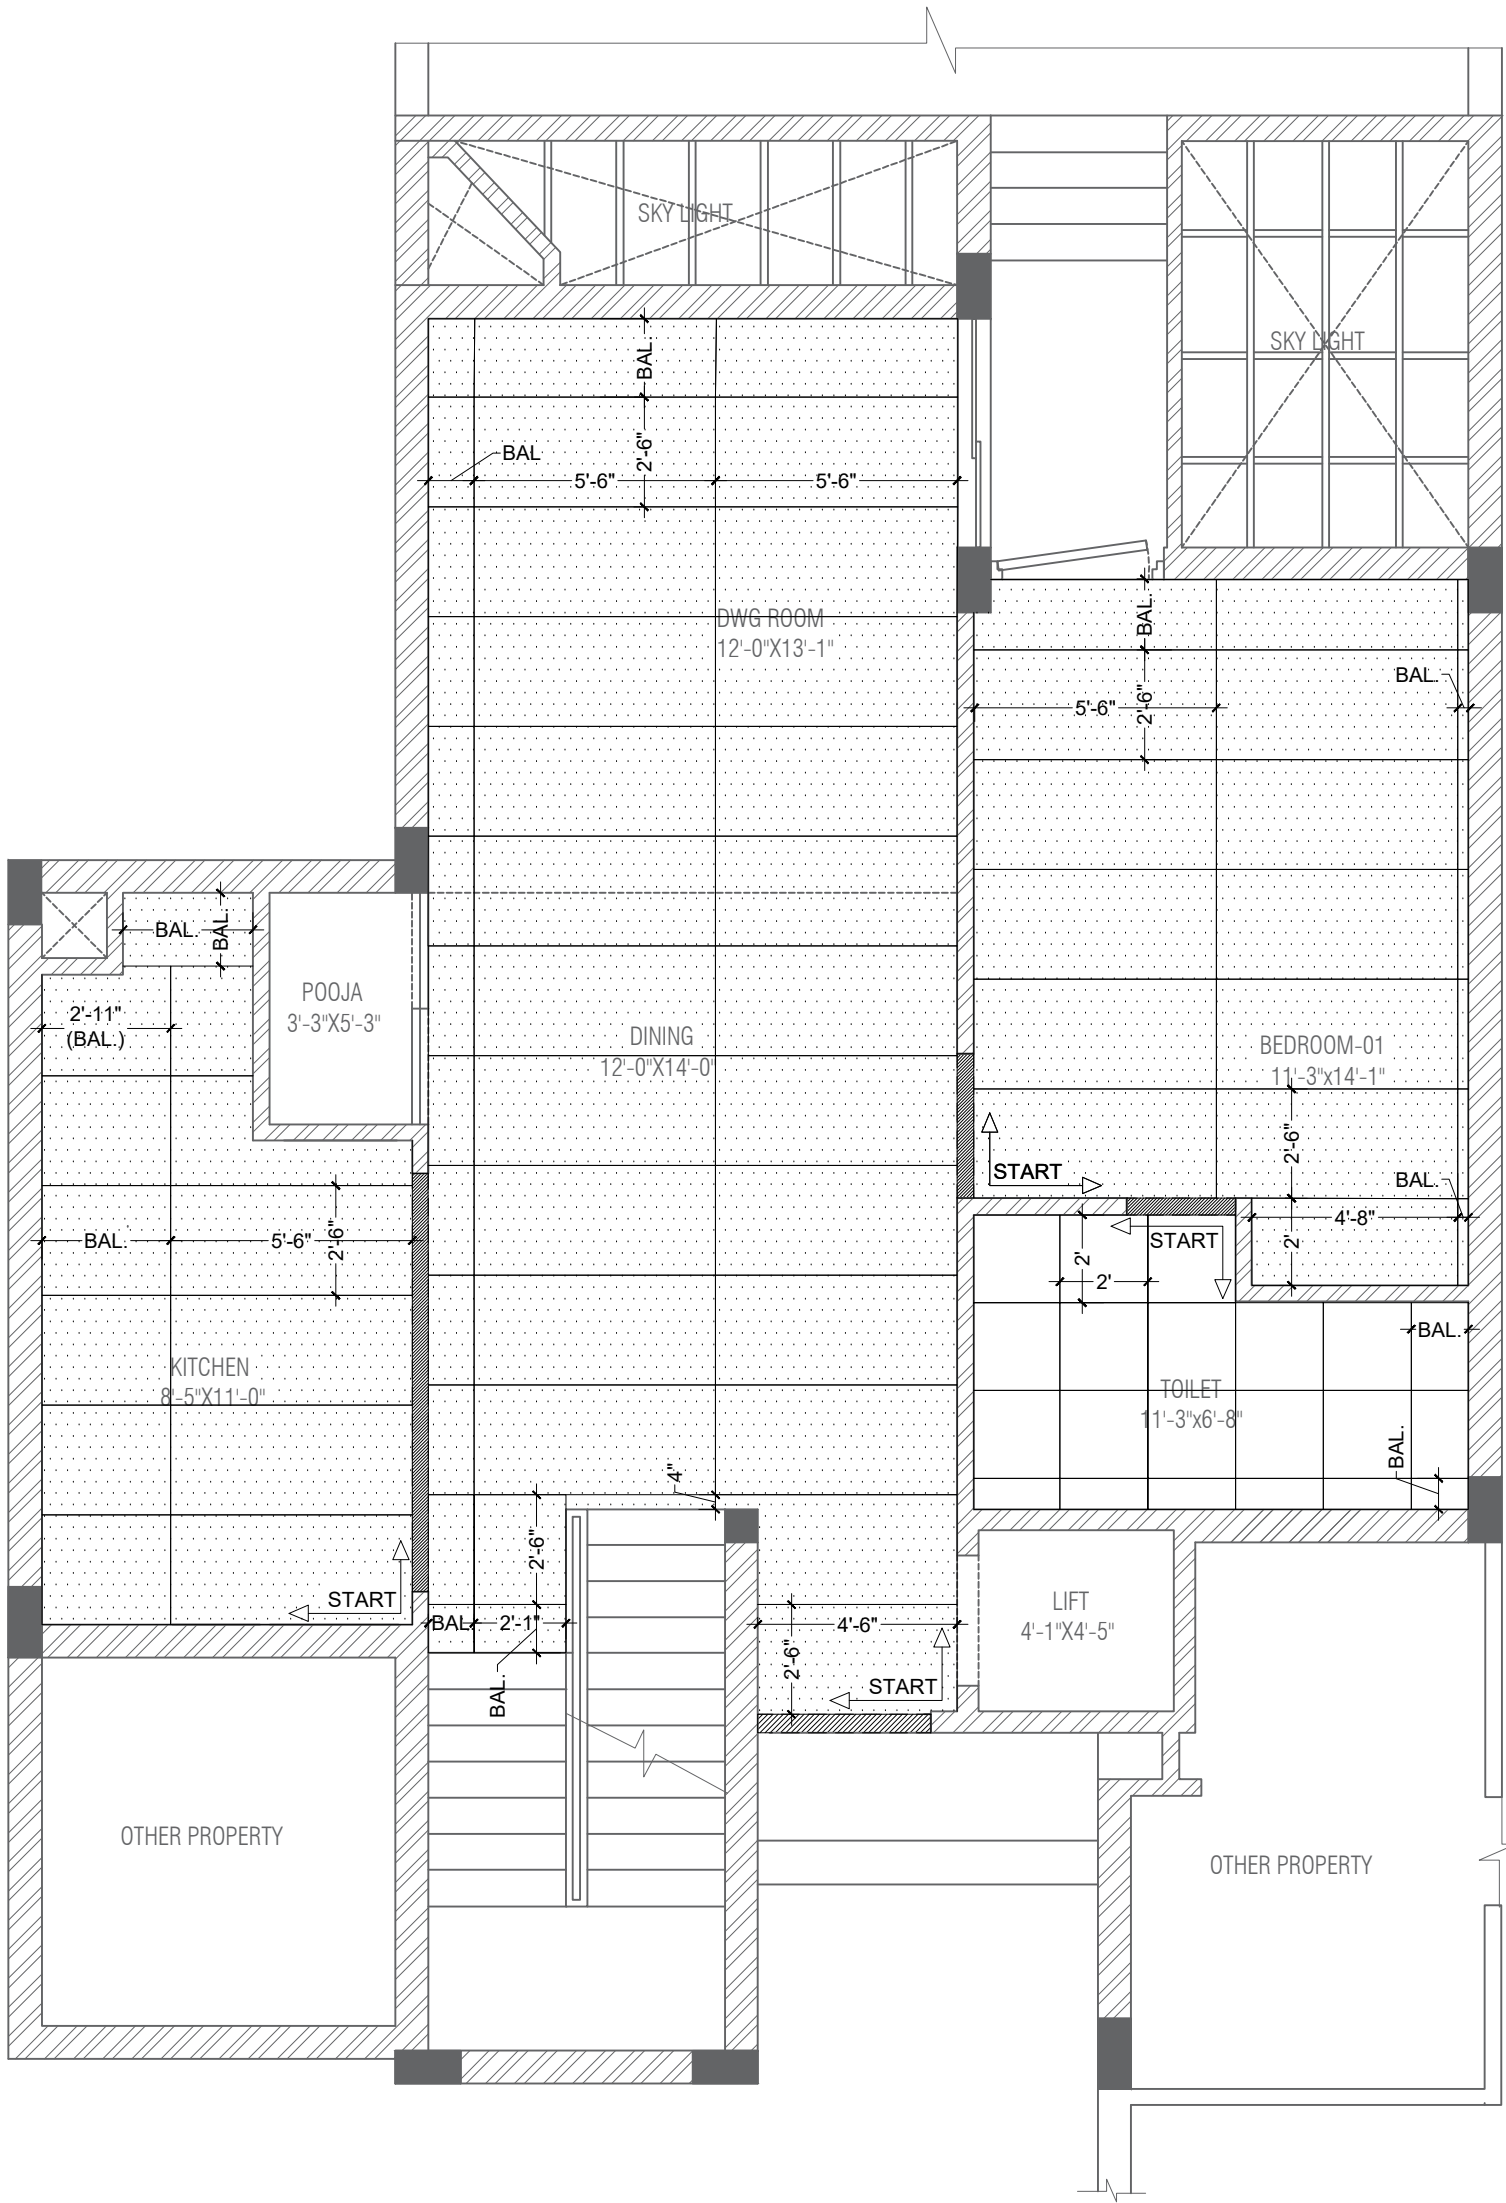

LEGEND		
S,NO	TILES	SIZE
1		2'-6" x "5'-6"
2		2' x 2'

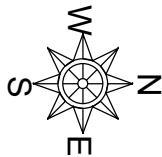

ARCHITECTS



Architects, Interior Designer, Landscape Designer, & Structural Designer
Head. Off: F-52, 1st Floor, Near Gurudwara, Madhu Vihar, JP Extension, Delhi-110092

Architect:

AR. PRABHAT ARYA

Sign:

Date:

Project Title:

**RESIDENCE
AT
RISE VILLA**

Drawing Title:

**GROUND FLOOR
PLUMBING LAYOUT PLAN**

Scale:

NTS

Date:

2026.04.16

Proj No:

—

Rev. No:

—

File Name:

—

Drawn:

SUMIT

Checked:


Ar. Yojna


Dwg No:


FL_1002

Rev. Date:

—

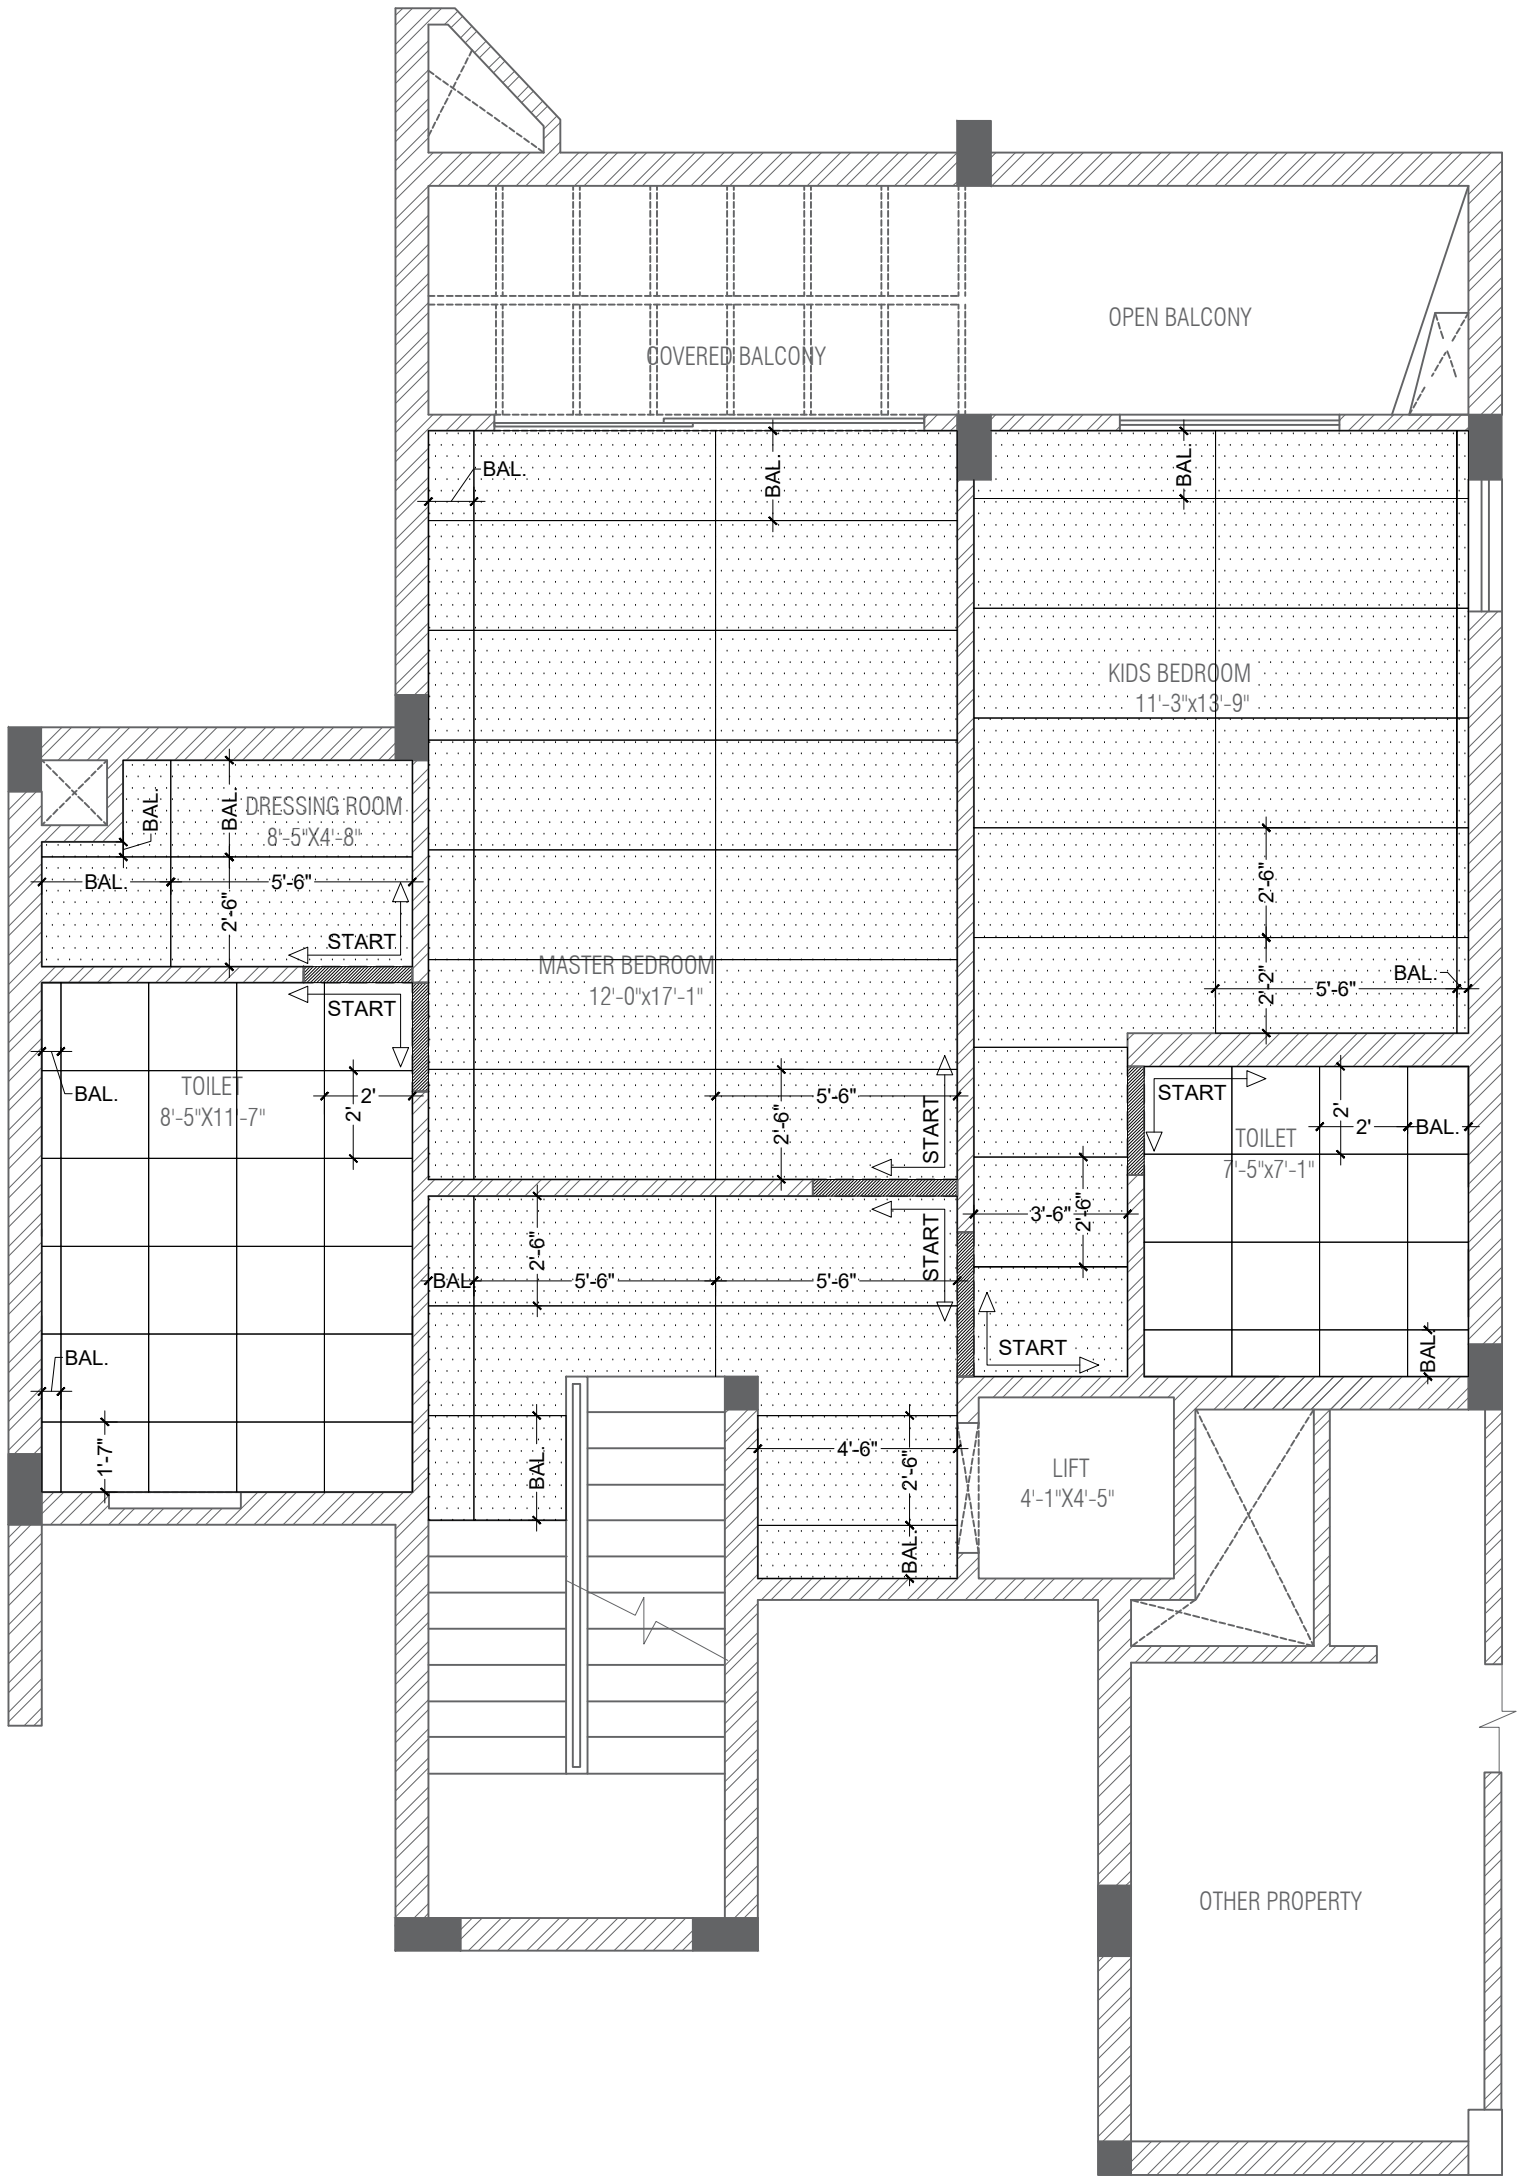

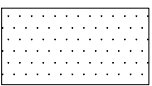LEGEND		
S,NO	TILES	SIZE
1		2'-6" x "5'-6"
2		2' x 2'

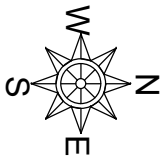

ARCHITECTS ARCHITECTSHIVE REDEFINING THE LIMITS OF ARCHITECTURE Architects, Interior Designer, Landscape Designer, & Structural Designer Head. Off: F-52, 1st Floor, Near Gurudwara, Madhu Vihar, J.P Extension, Delhi-110092	Architect: AR. PRABHAT ARYA		Project Title: RESIDENCE AT RISE VILLA	Drawing Title: FIRST FLOOR PLUMBING LAYOUT PLAN	Scale:	NTS	Drawn:	SUMIT		
	Sign: _____ Date: _____				Date:	2026.04.16	Checked:	Ar. Yajna		
					Proj No:	—	Dwg No:	FL_1003		
					Rev. No:		Rev. Date:	—		
					File Name:	—				